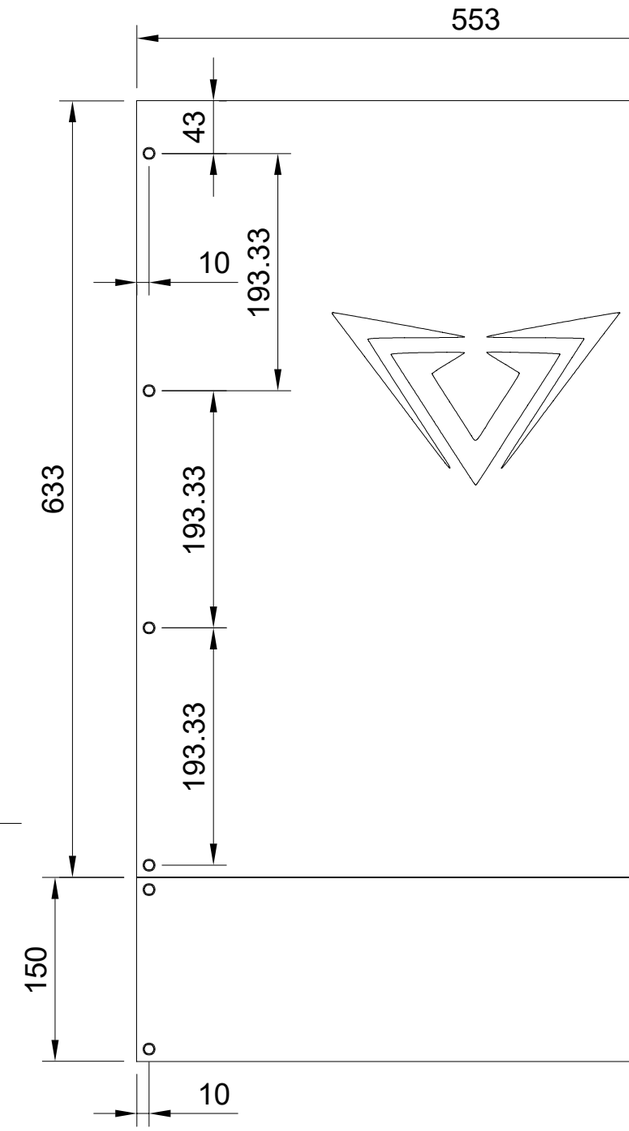

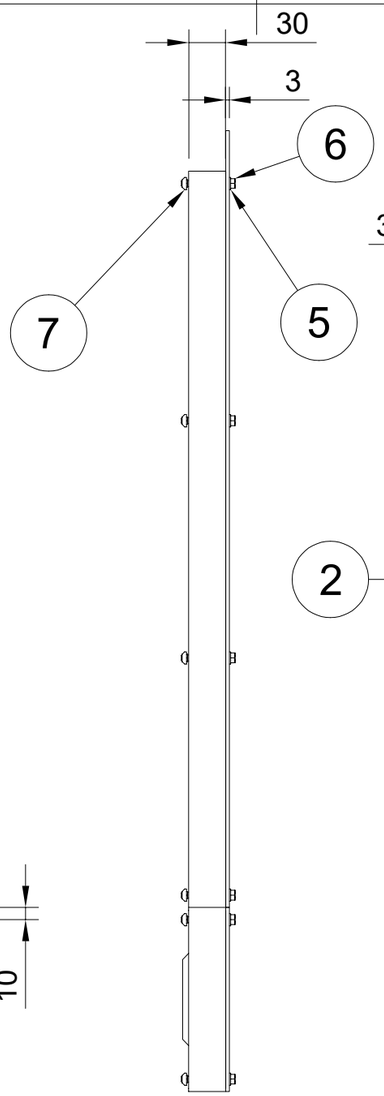

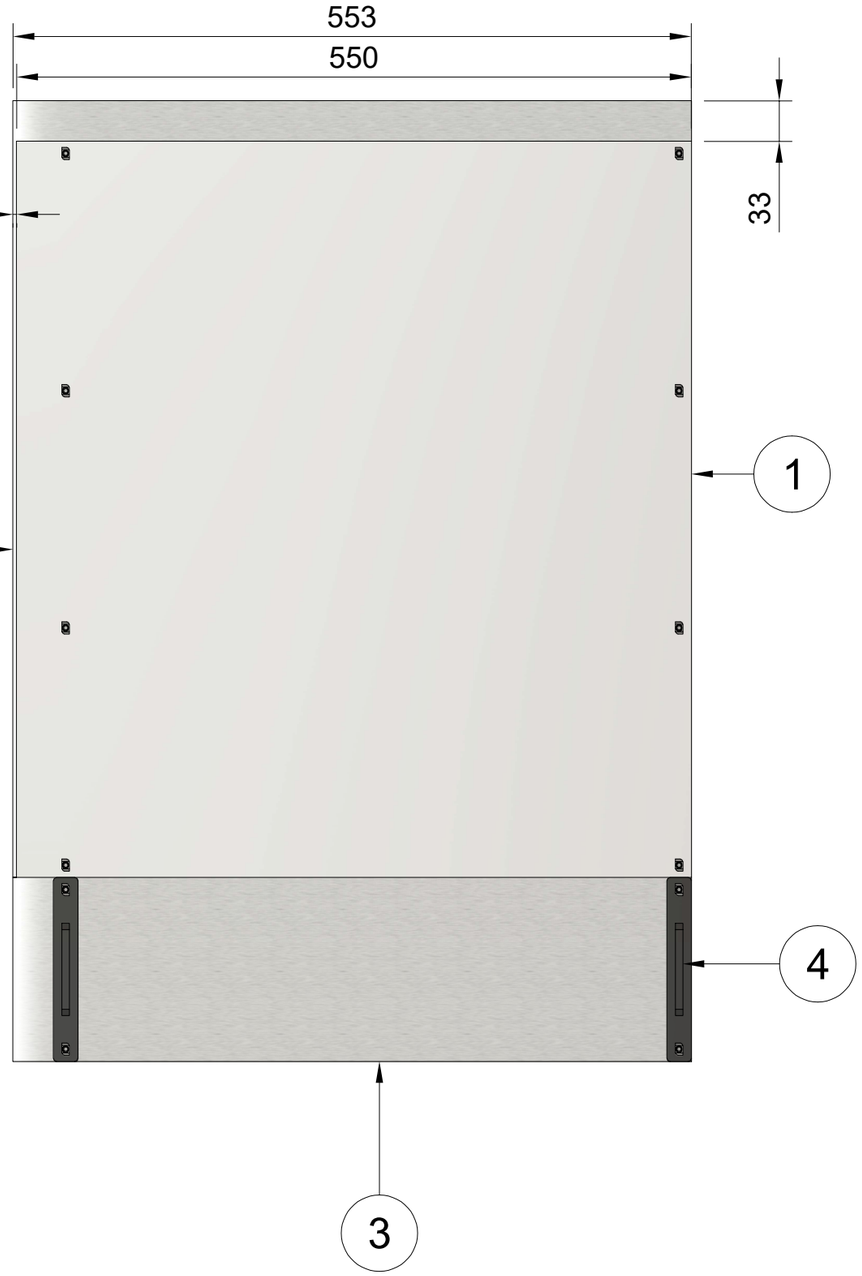

Parts List		
Item	Qty	Part Number
1	1	V2 Insulation Side B
2	1	V2 Panel Side B Upper
3	1	V2 Panel Side B Lower
4	2	V2 Insulation Spacer
5	12	M5 WASHER DIN 125
6	12	M5x40 HEX DIN 931
7	12	M5 Nut Hammer Nut

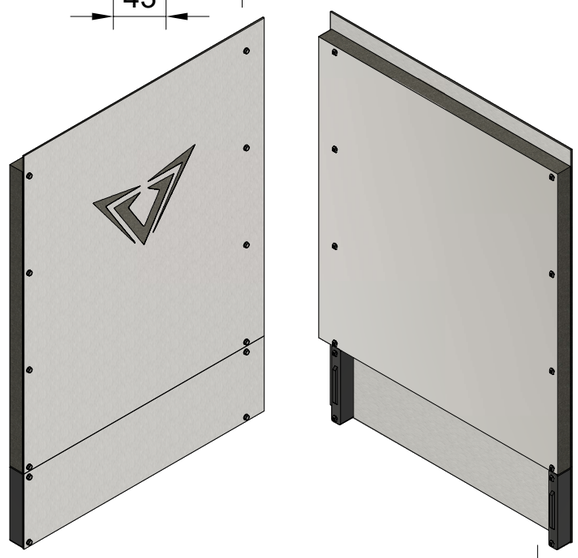

	Drawn By Roy Berntsen	Part Name V2 Panel Side B	pro 3d
REV. V2 BETA	Scale 1:10	Date 04/04/2026	